Project Management Initials: Designer: JB Checked: AA Approved: NB ISO A1 594mm x 841mm

Last saved by: JOSEPH.BOYMAN(2020-06-11) Last Plotted: 2020-06-12
Filename: Y:\60515228 - ASH ROAD BRIDGE\WORKING\CAD\DRAWING\DRAWINGS\ASHB-ACM-AH-00-DR-CE-00002.DWG

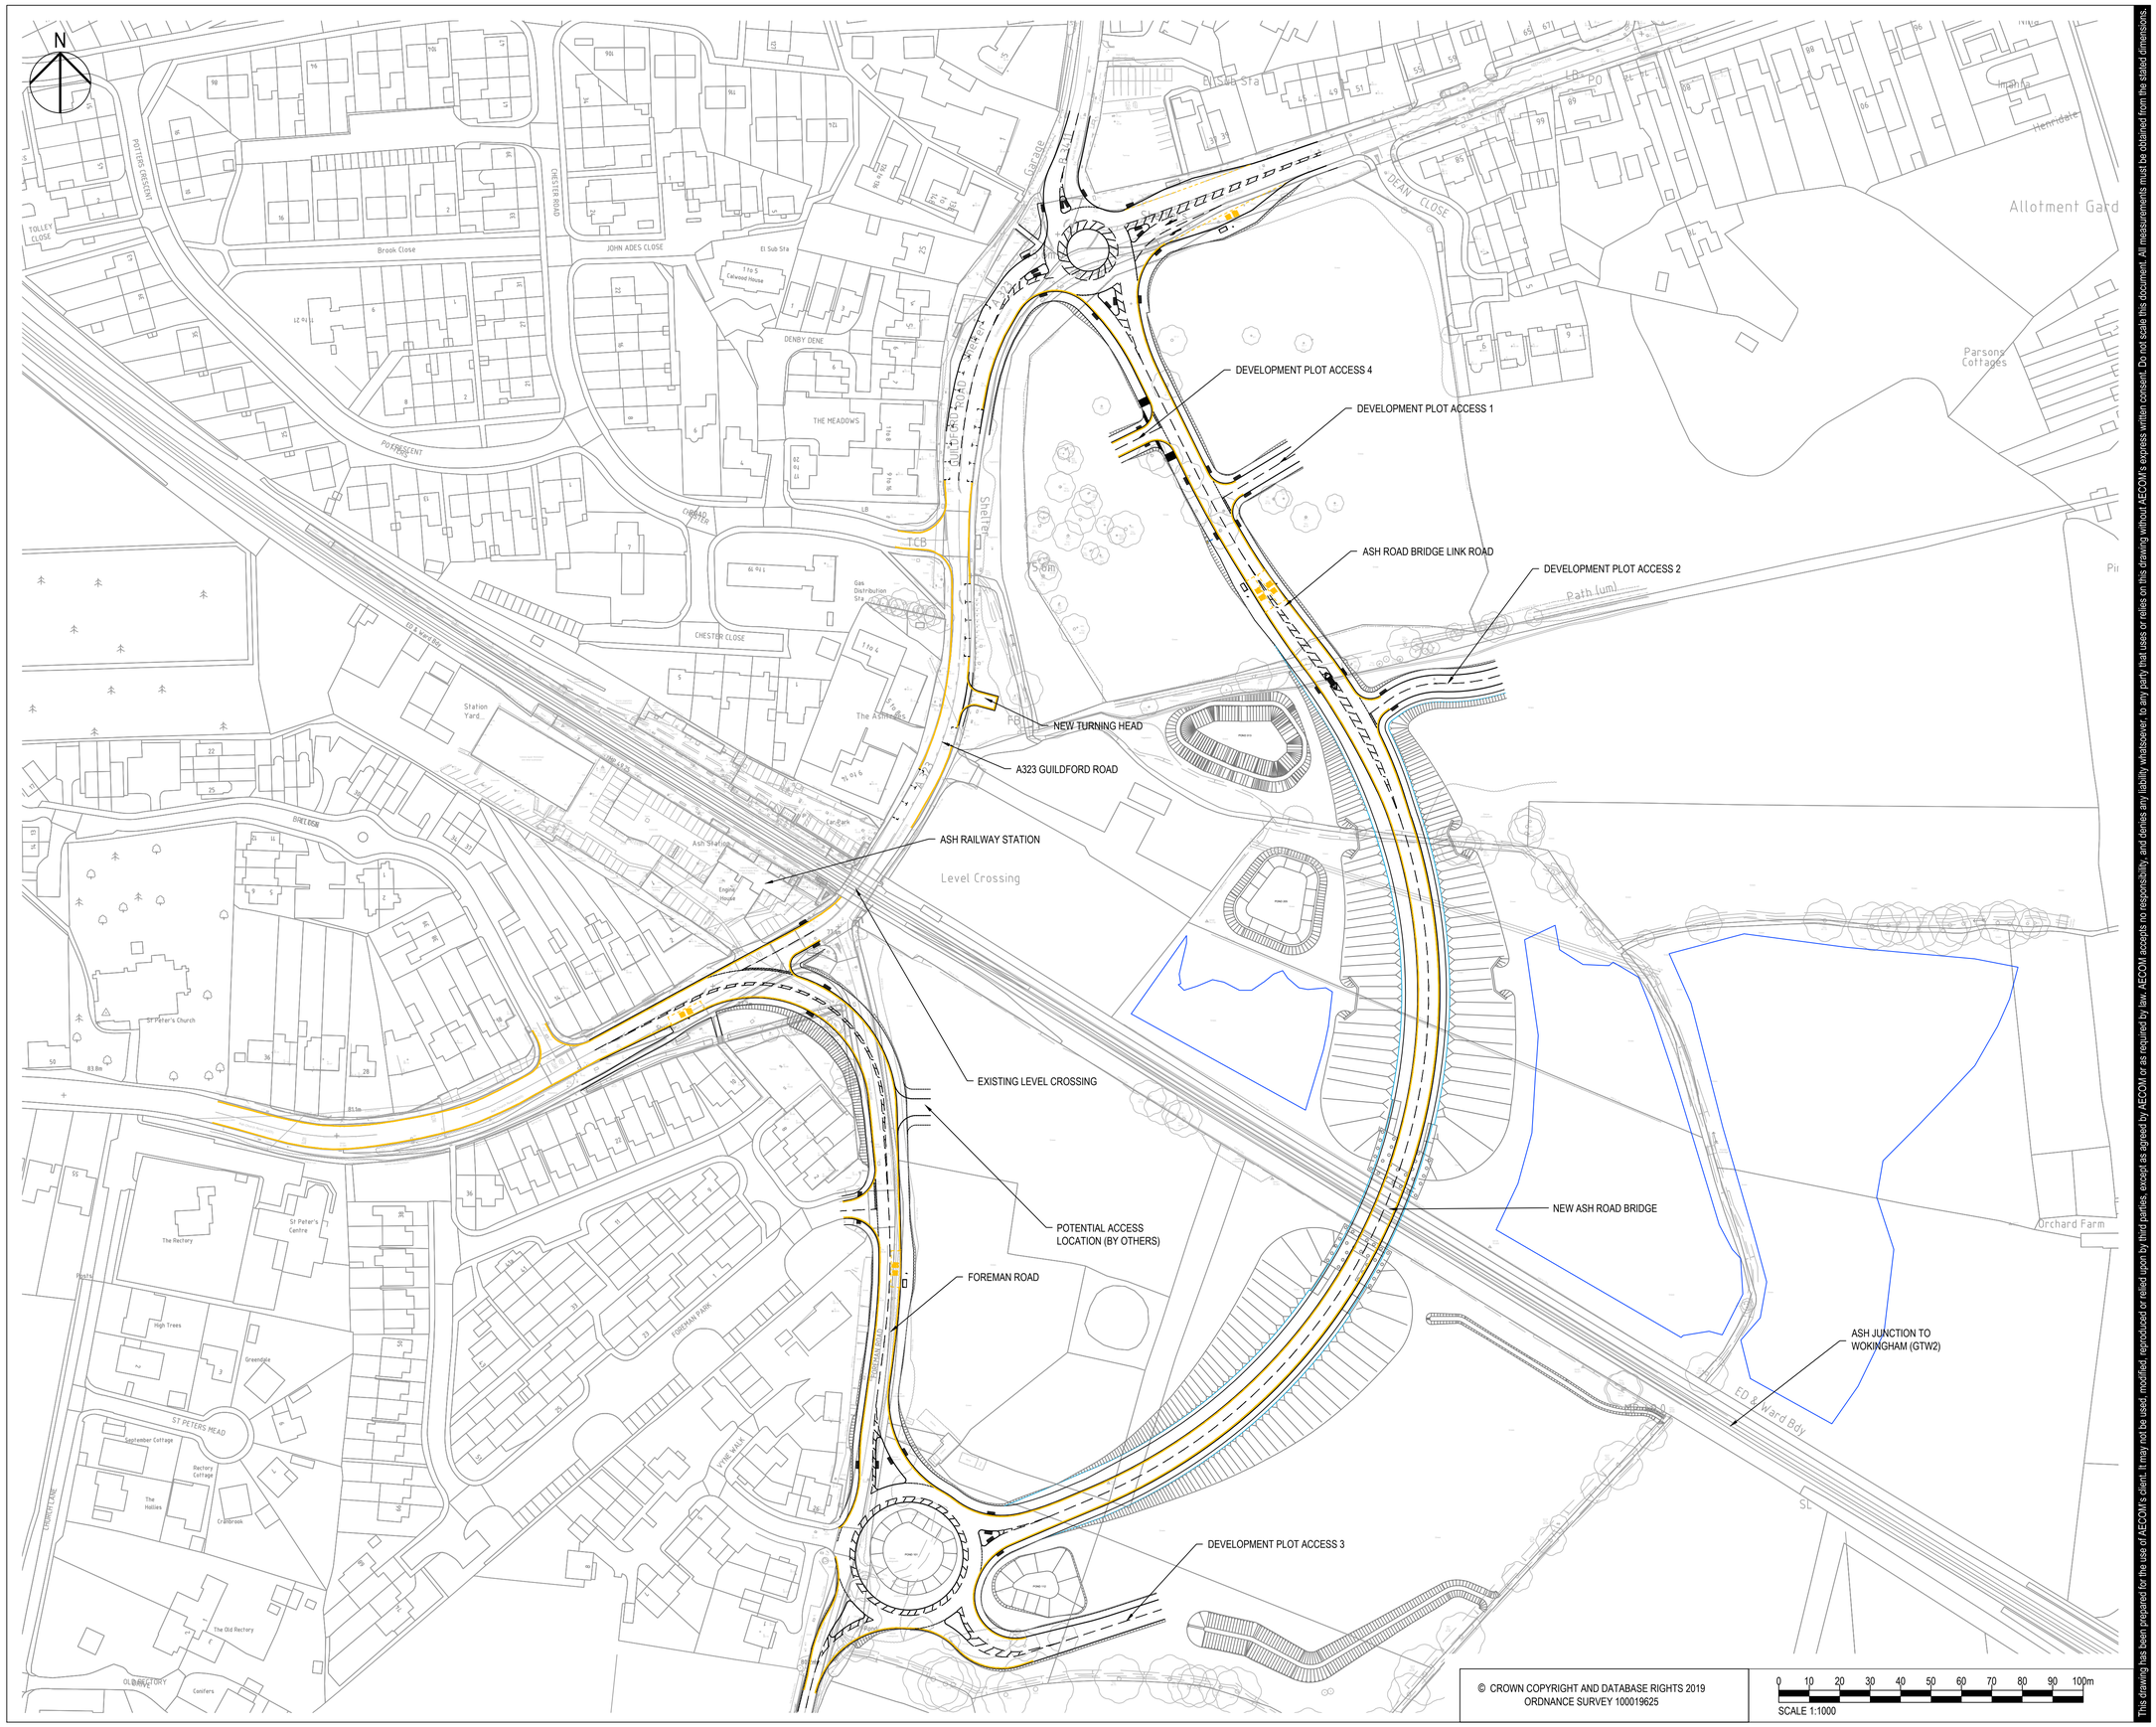

This drawing has been prepared for the use of AECOM's client. It may not be used, modified, reproduced or relied upon by third parties, except as agreed by AECOM or as required by law. AECOM accepts no responsibility, and denies any liability whatsoever, to any party that uses or relies on this drawing without AECOM's express written consent. Do not scale this document. All measurements must be obtained from the stated dimensions.

AECOM

PROJECT

ASH ROAD BRIDGE

CLIENT

Guildford Borough Council

CONSULTANT

AECOM Infrastructure & Environment UK Ltd
Midpoint, Alecon Link,
Basingstoke, Hampshire, RG21 7PP
+44 (0)1256 310 200 tel
+44 (0)1256 310 201 fax
www.aecom.com

GENERAL NOTES

1. THIS DRAWING IS TO BE READ IN CONJUNCTION WITH ALL RELEVANT ARCHITECTS, ENGINEERS,SERVICES AND SPECIALIST DRAWINGS AND SPECIFICATION.
2. ANY DISCREPANCIES IN DIMENSIONS OR DETAILS ON OR BETWEEN THESE DRAWINGS SHOULD BE DRAWN TO THE ATTENTION OF THE ARCHITECT AND/OR THE ENGINEER FOR CLARIFICATION.
3. ALL DIMENSIONS ARE IN METRES UNLESS NOTED OTHERWISE.
4. DO NOT SCALE THIS DRAWING.

ISSUE/REVISION

I/R	DATE	DESCRIPTION
P08	07.05.2020	FINAL PLANNING SUBMISSION
P07	16.08.2019	ISSUED FOR PLANNING
P06	09.07.2019	FINAL DRAFT
P05	15.05.2019	LINK ROAD ACCESS REVISED
P04	01.04.2019	FOREMAN ROAD REVISED
P03	15.03.2019	ISSUED FOR AIP
P02	18.02.2019	GUILDFORD ROAD REVISED
P01	14.12.2018	FIRST ISSUE

PROJECT NUMBER

60515228

SHEET TITLE

OVERALL SITE PLAN
GENERAL ARRANGEMENT

SHEET NUMBER

ASHB-ACM-AH-00-DR-CE-00002