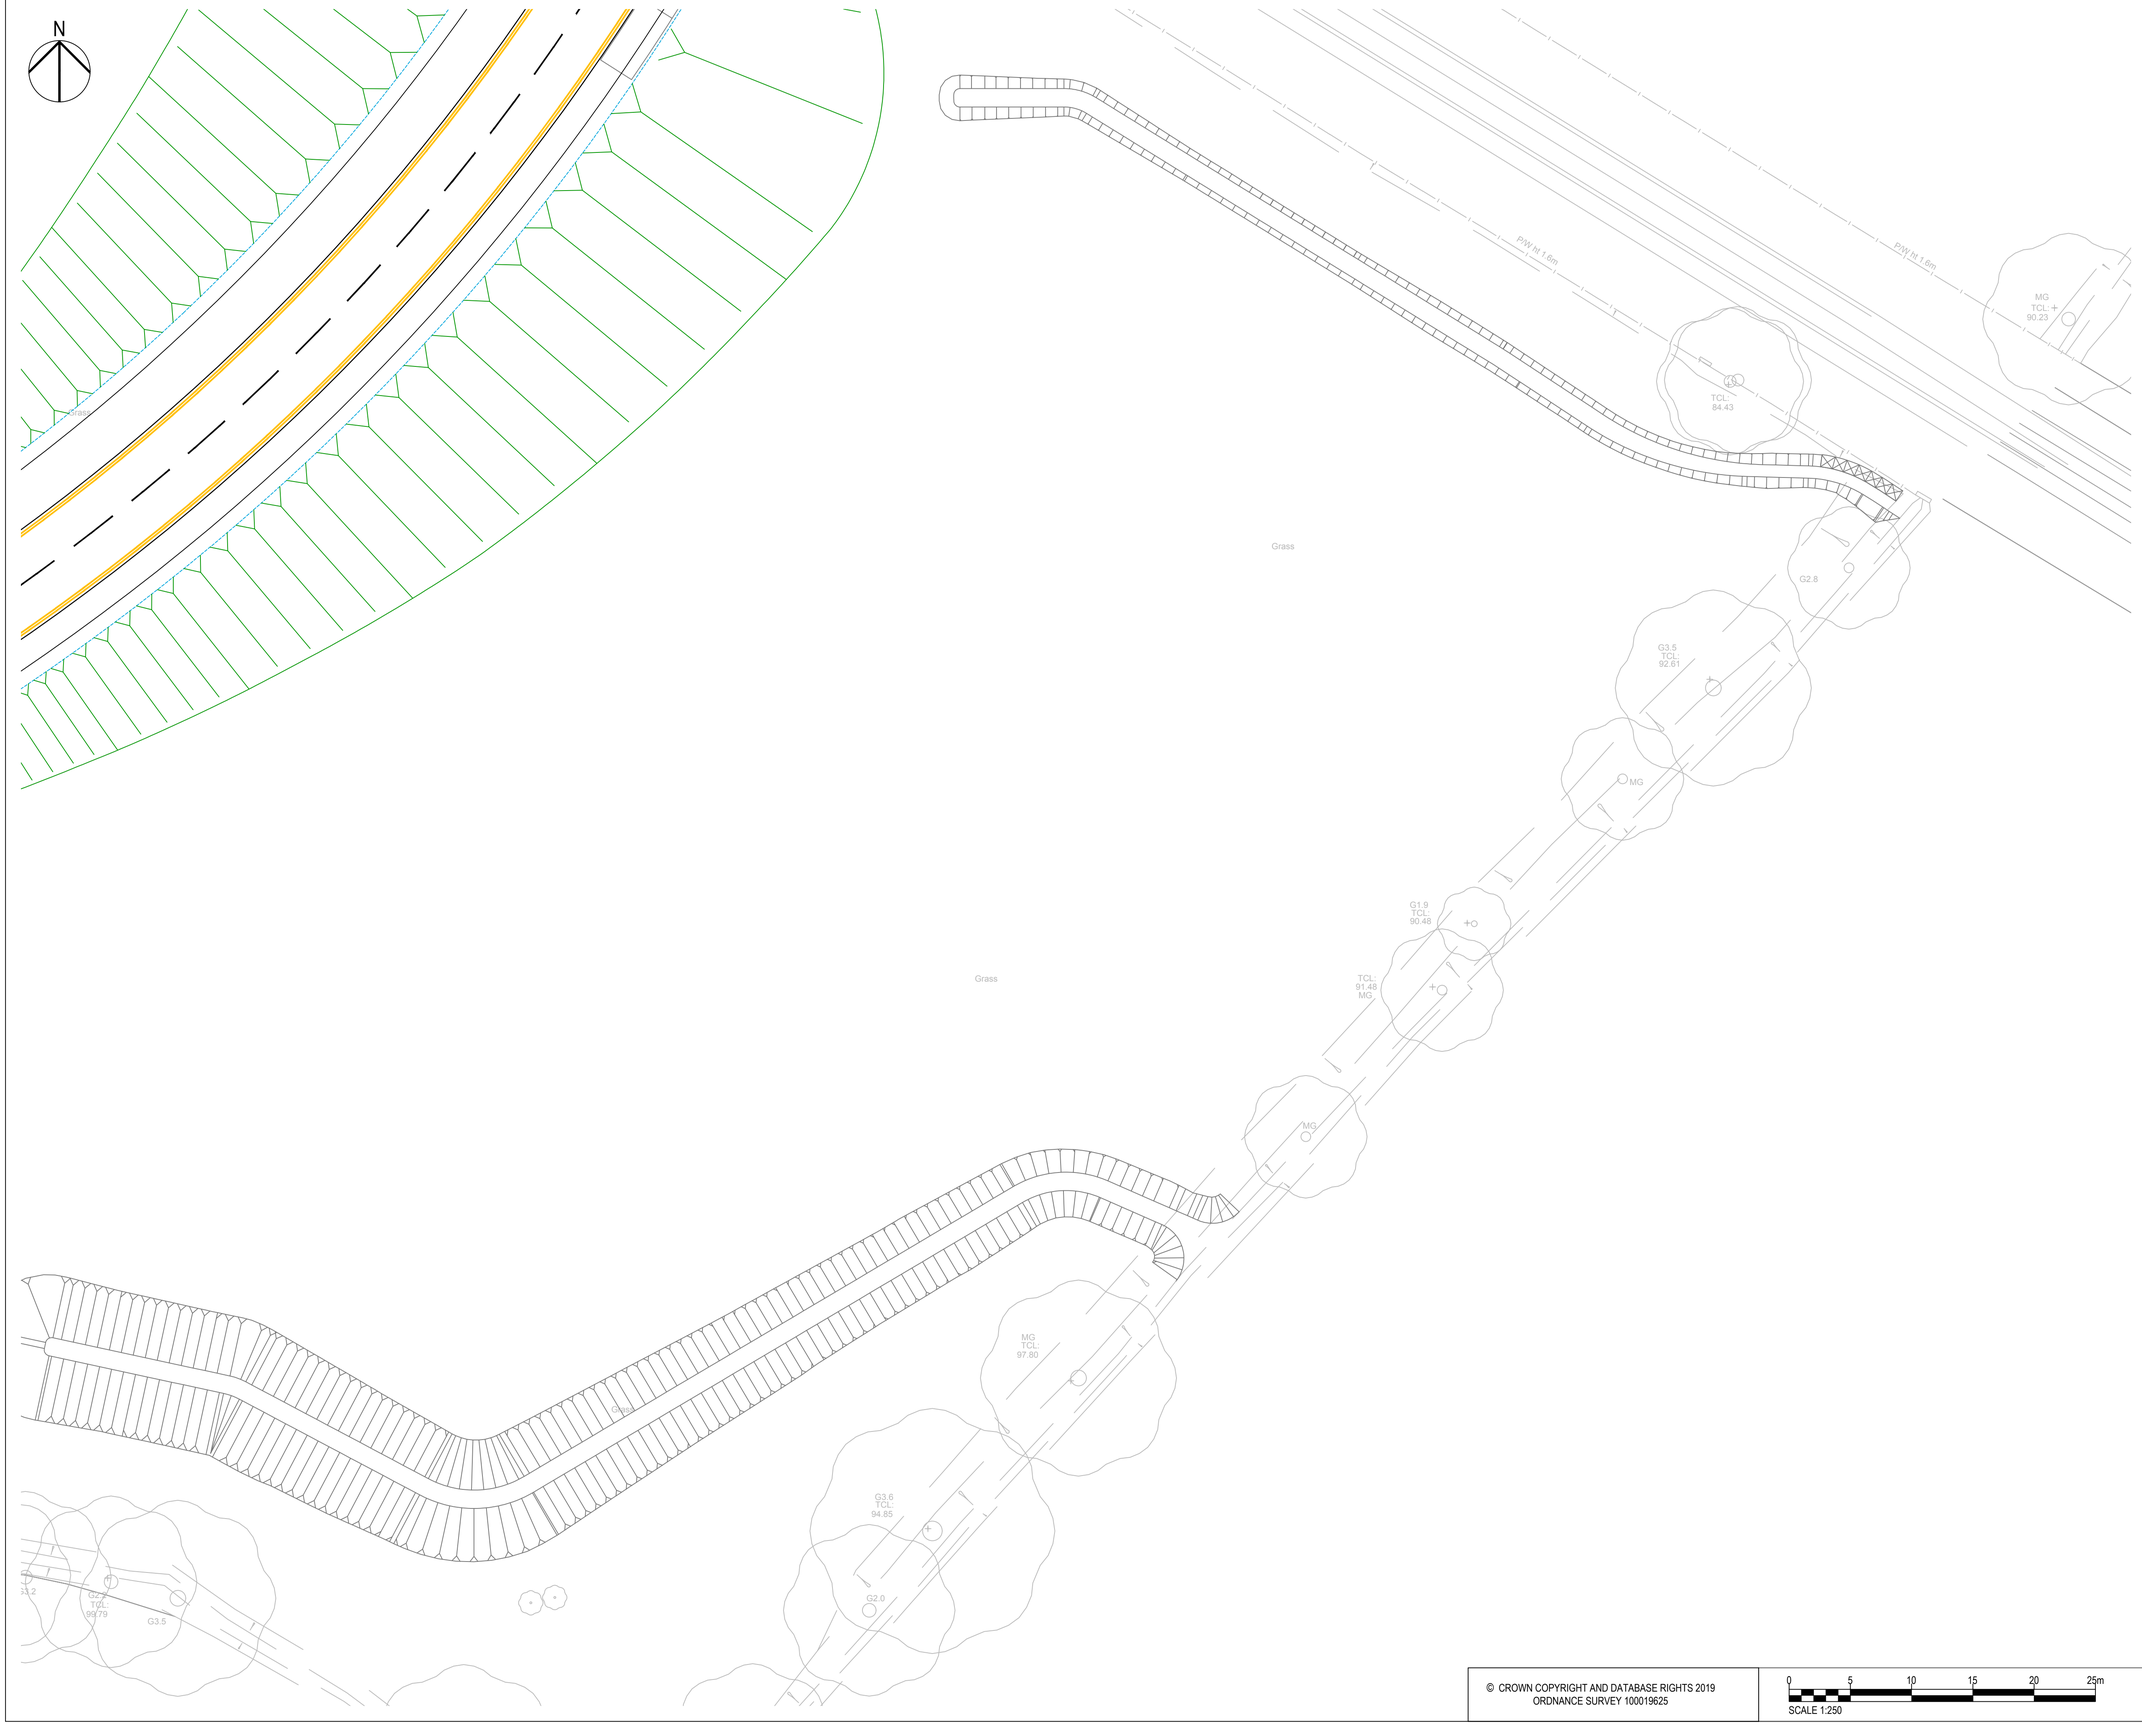

© CROWN COPYRIGHT AND DATABASE RIGHTS 2019
ORDNANCE SURVEY 100019625

0 5 10 15 20 25m
SCALE 1:250

This drawing has been prepared for the use of AECOM's client. It may not be used, modified, reproduced or relied upon by third parties, except as agreed by AECOM or as required by law. AECOM accepts no responsibility, and denies any liability whatsoever, to any party that uses or relies on this drawing without AECOM's express written consent. Do not scale this document. All measurements must be obtained from the stated dimensions.

AECOM

PROJECT

ASH ROAD BRIDGE

CLIENT

Guildford Borough Council

CONSULTANT

AECOM Infrastructure & Environment UK Ltd
Midpoint, Alecon Link,
Basingstoke, Hampshire, RG21 7PP
+44 (0)1256 310 200 tel
+44 (0)1256 310 201 fax
www.aecom.com

GENERAL NOTES

1. THIS DRAWING IS TO BE READ IN CONJUNCTION WITH ALL RELEVANT ARCHITECTS, ENGINEERS,SERVICES AND SPECIALIST DRAWINGS AND SPECIFICATION.
2. ANY DISCREPANCIES IN DIMENSIONS OR DETAILS ON OR BETWEEN THESE DRAWINGS SHOULD BE DRAWN TO THE ATTENTION OF THE ARCHITECT AND/OR THE ENGINEER FOR CLARIFICATION.
3. ALL DIMENSIONS ARE IN METRES UNLESS NOTED OTHERWISE.
4. DO NOT SCALE THIS DRAWING.
5. AS AGREED WITH SURREY COUNCIL COUNCIL THE HIGHWAY BOUNDARY WILL BE AT THE BACK OF THE FOOTWAY WHERE ADJACENT DEVELOPMENT FRONTS THE ROAD AND WHERE DEVELOPMENT LEVELS ARE RAISED TO SUIT THE ROAD LEVELS.
6. 6. FINAL LEVELS SUBJECT TO DETAILED DESIGN AND TECHNICAL APPROVAL BY SURREY COUNTY COUNCIL AND NETWORK RAIL.

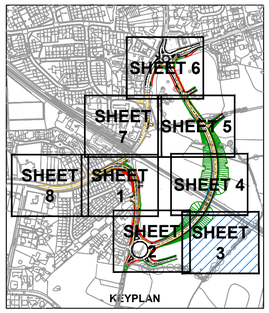

KEY

- CUT SLOPE
- FILL SLOPE
- 5.200 HIGHWAY GEOMETRY
- R23.500 ROUNDABOUT ENTRY PATH RADIUS
- 81.2° ROUNDABOUT ENTRY ANGLE

ISSUE/REVISION

I/R	DATE	DESCRIPTION
P03	16.08.2019	ISSUED FOR PLANNING
P02	09.07.2019	FINAL DRAFT
P01	20.05.2019	FIRST ISSUE

PROJECT NUMBER

605125228

SHEET TITLE

GEOMETRIC DESIGN LAYOUT

SHEET 3

SHEET NUMBER

ASHB-ACM-AH-01-DR-CE-07003

Project Management Initials: Designer: JB Checked: AA Approved: NB ISO A1 594mm x 841mm
Last saved by: MATT.HALTON(2019-08-15) Last Plotted: 2019-08-15
Filename: Y:\605\15228 - ASH ROAD BRIDGE\WORKING\CAD\DRAWING\DRAWINGS\ASHB-ACM-AH-01-DR-CE-07003.DWG